


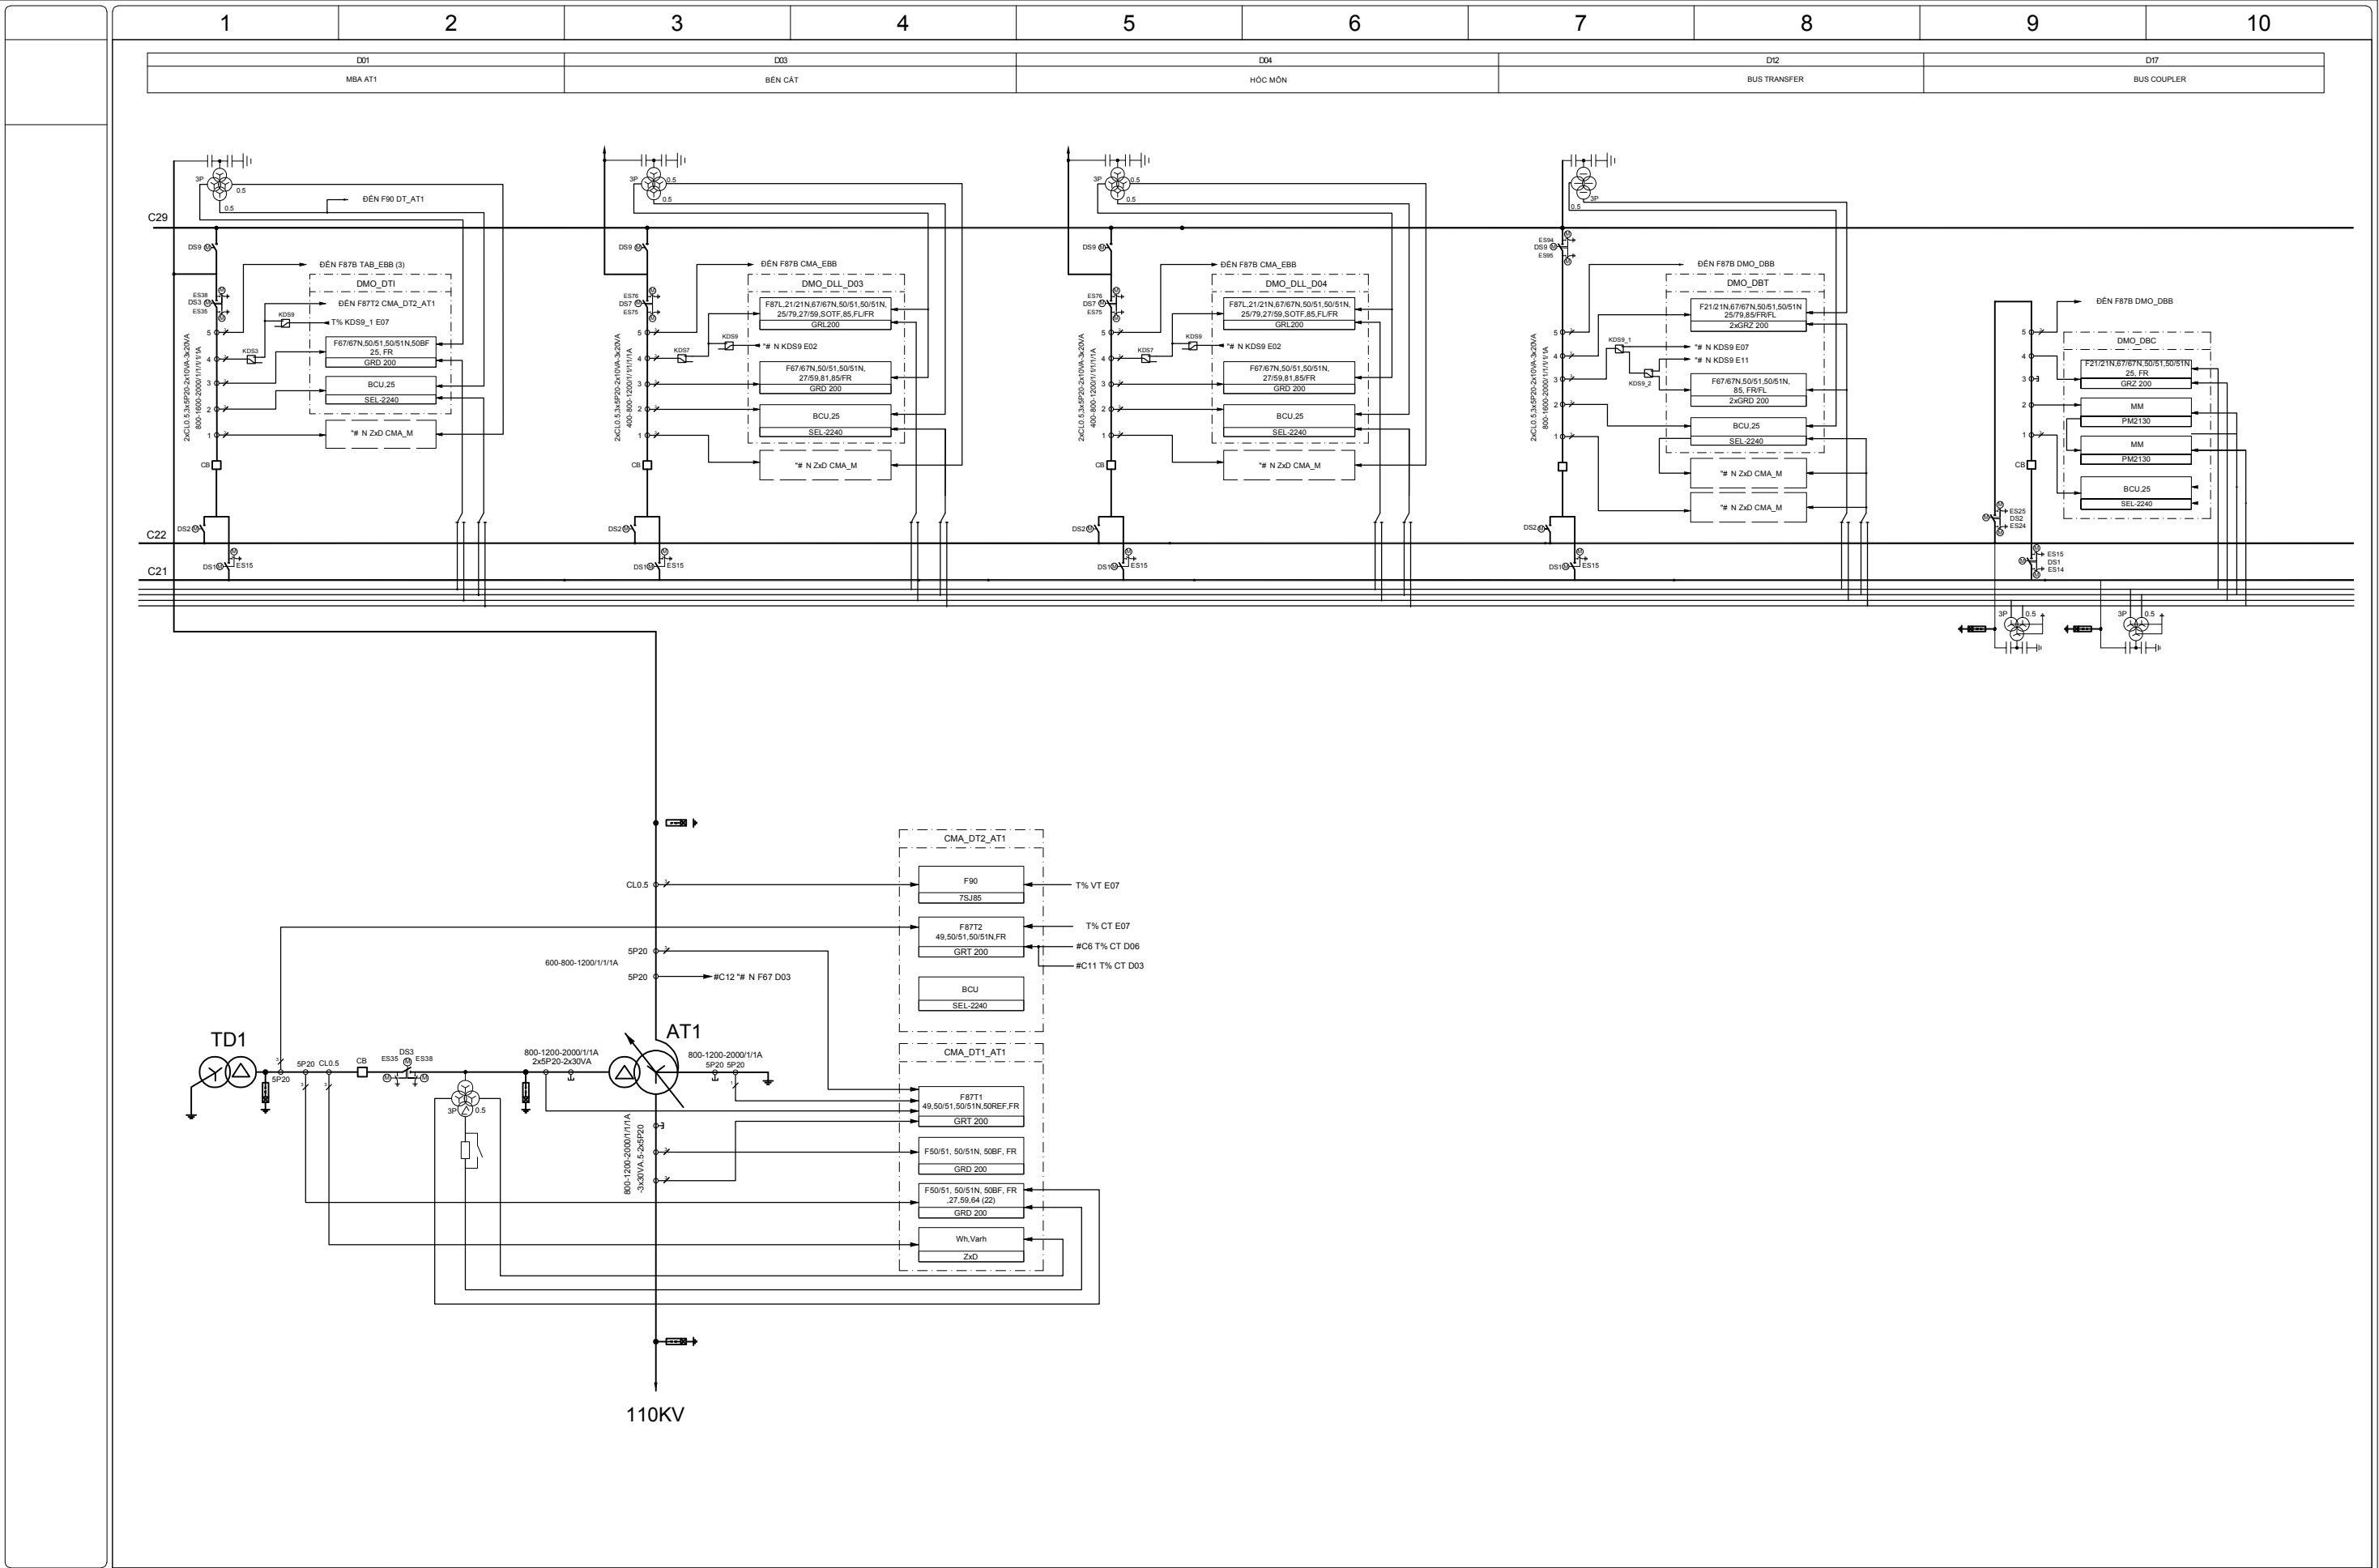

Rev	Revision description	Drawn date	Drawn by	Checked date	Checked by
A1	BASIC DESIGN	18.03.25		18.03.25	




SƠ ĐỒ PHƯƠNG THỨC ĐIỀU KHIỂN VÀ BẢO VỆ
PHÍA 220kV

Project. TRẠM BIẾN ÁP 220kV DEMO
VÀ ĐƯỜNG DÂY ĐẦU NỐI

Job No.
PECC3-25-07

Drawing No.
DMO_SL

=
+
Page 2
of 2

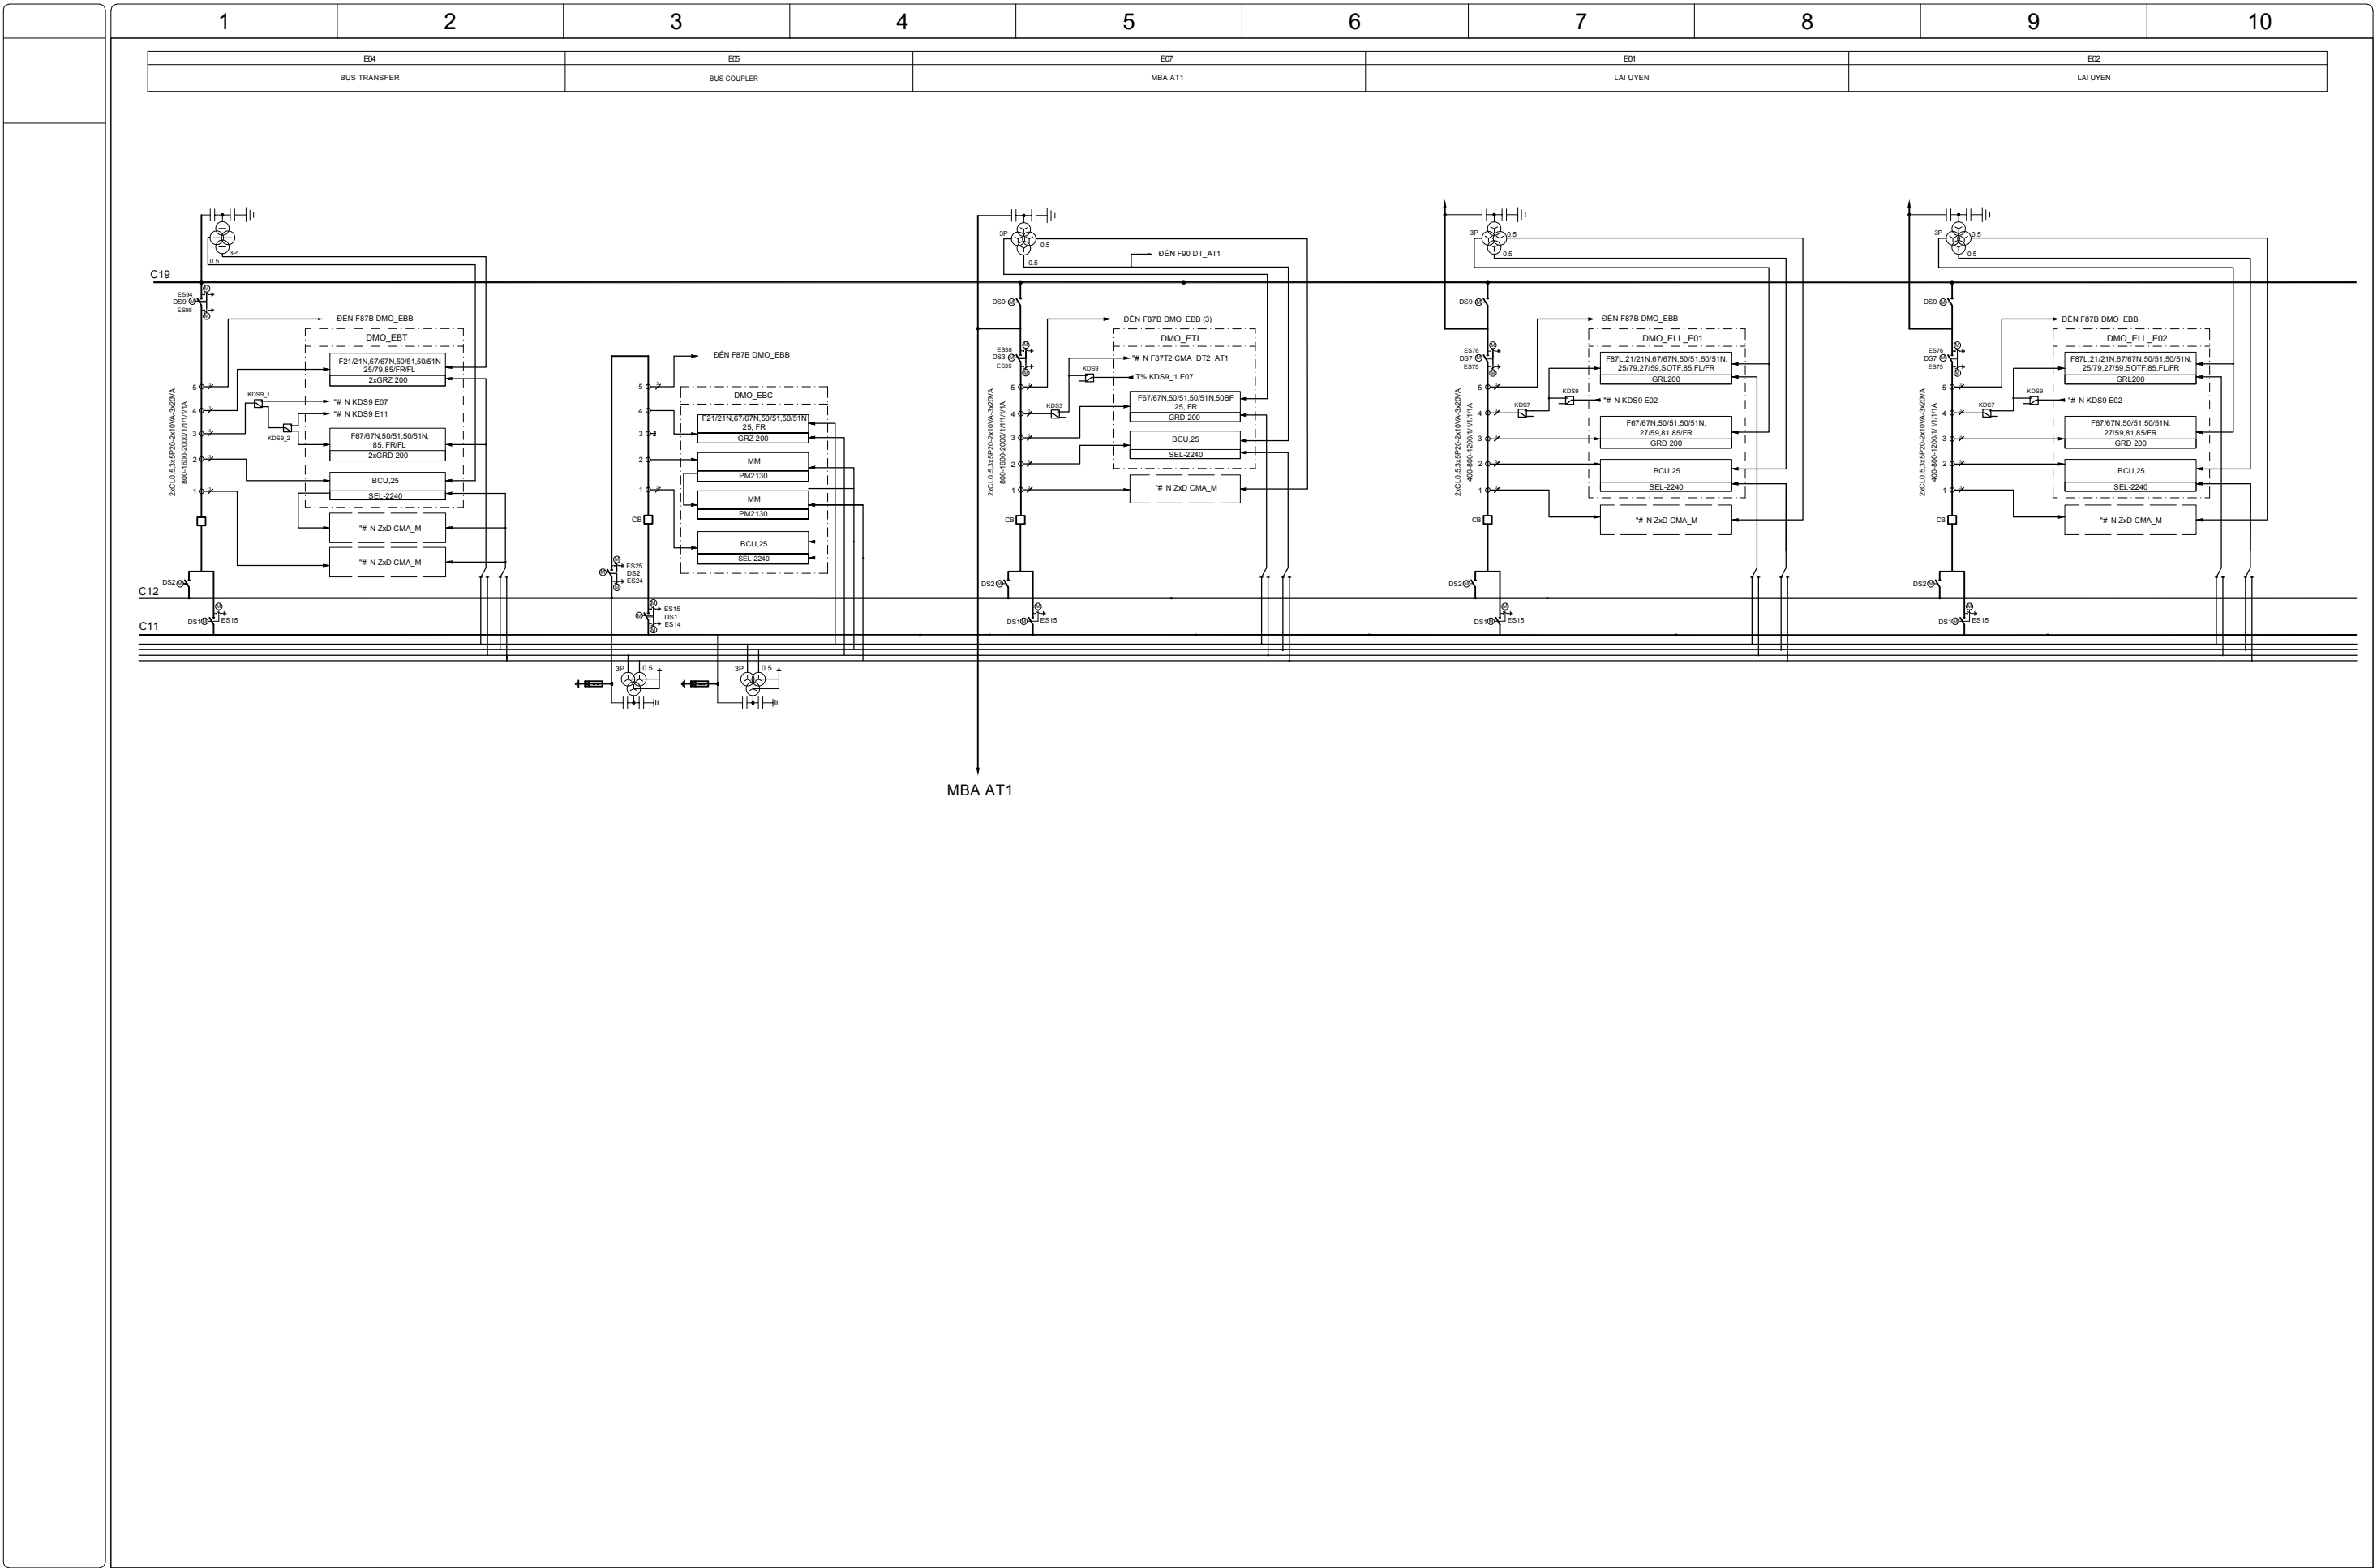

Rev	Revision description	Drawn date	Drawn by	Checked date	Checked by
A1	BASIC DESIGN	18.03.25		18.03.25	



SƠ ĐỒ PHƯƠNG THỨC ĐIỀU KHIỂN VÀ BẢO VỆ
PHÍA 110kV

Project. TRẠM BIẾN ÁP 220kV DEMO VÀ ĐƯỜNG DÂY ĐẦU NỒI		=
Job No. PECC3-25-07	Drawing No. DMO_SL	+
		Page 2
		of 2